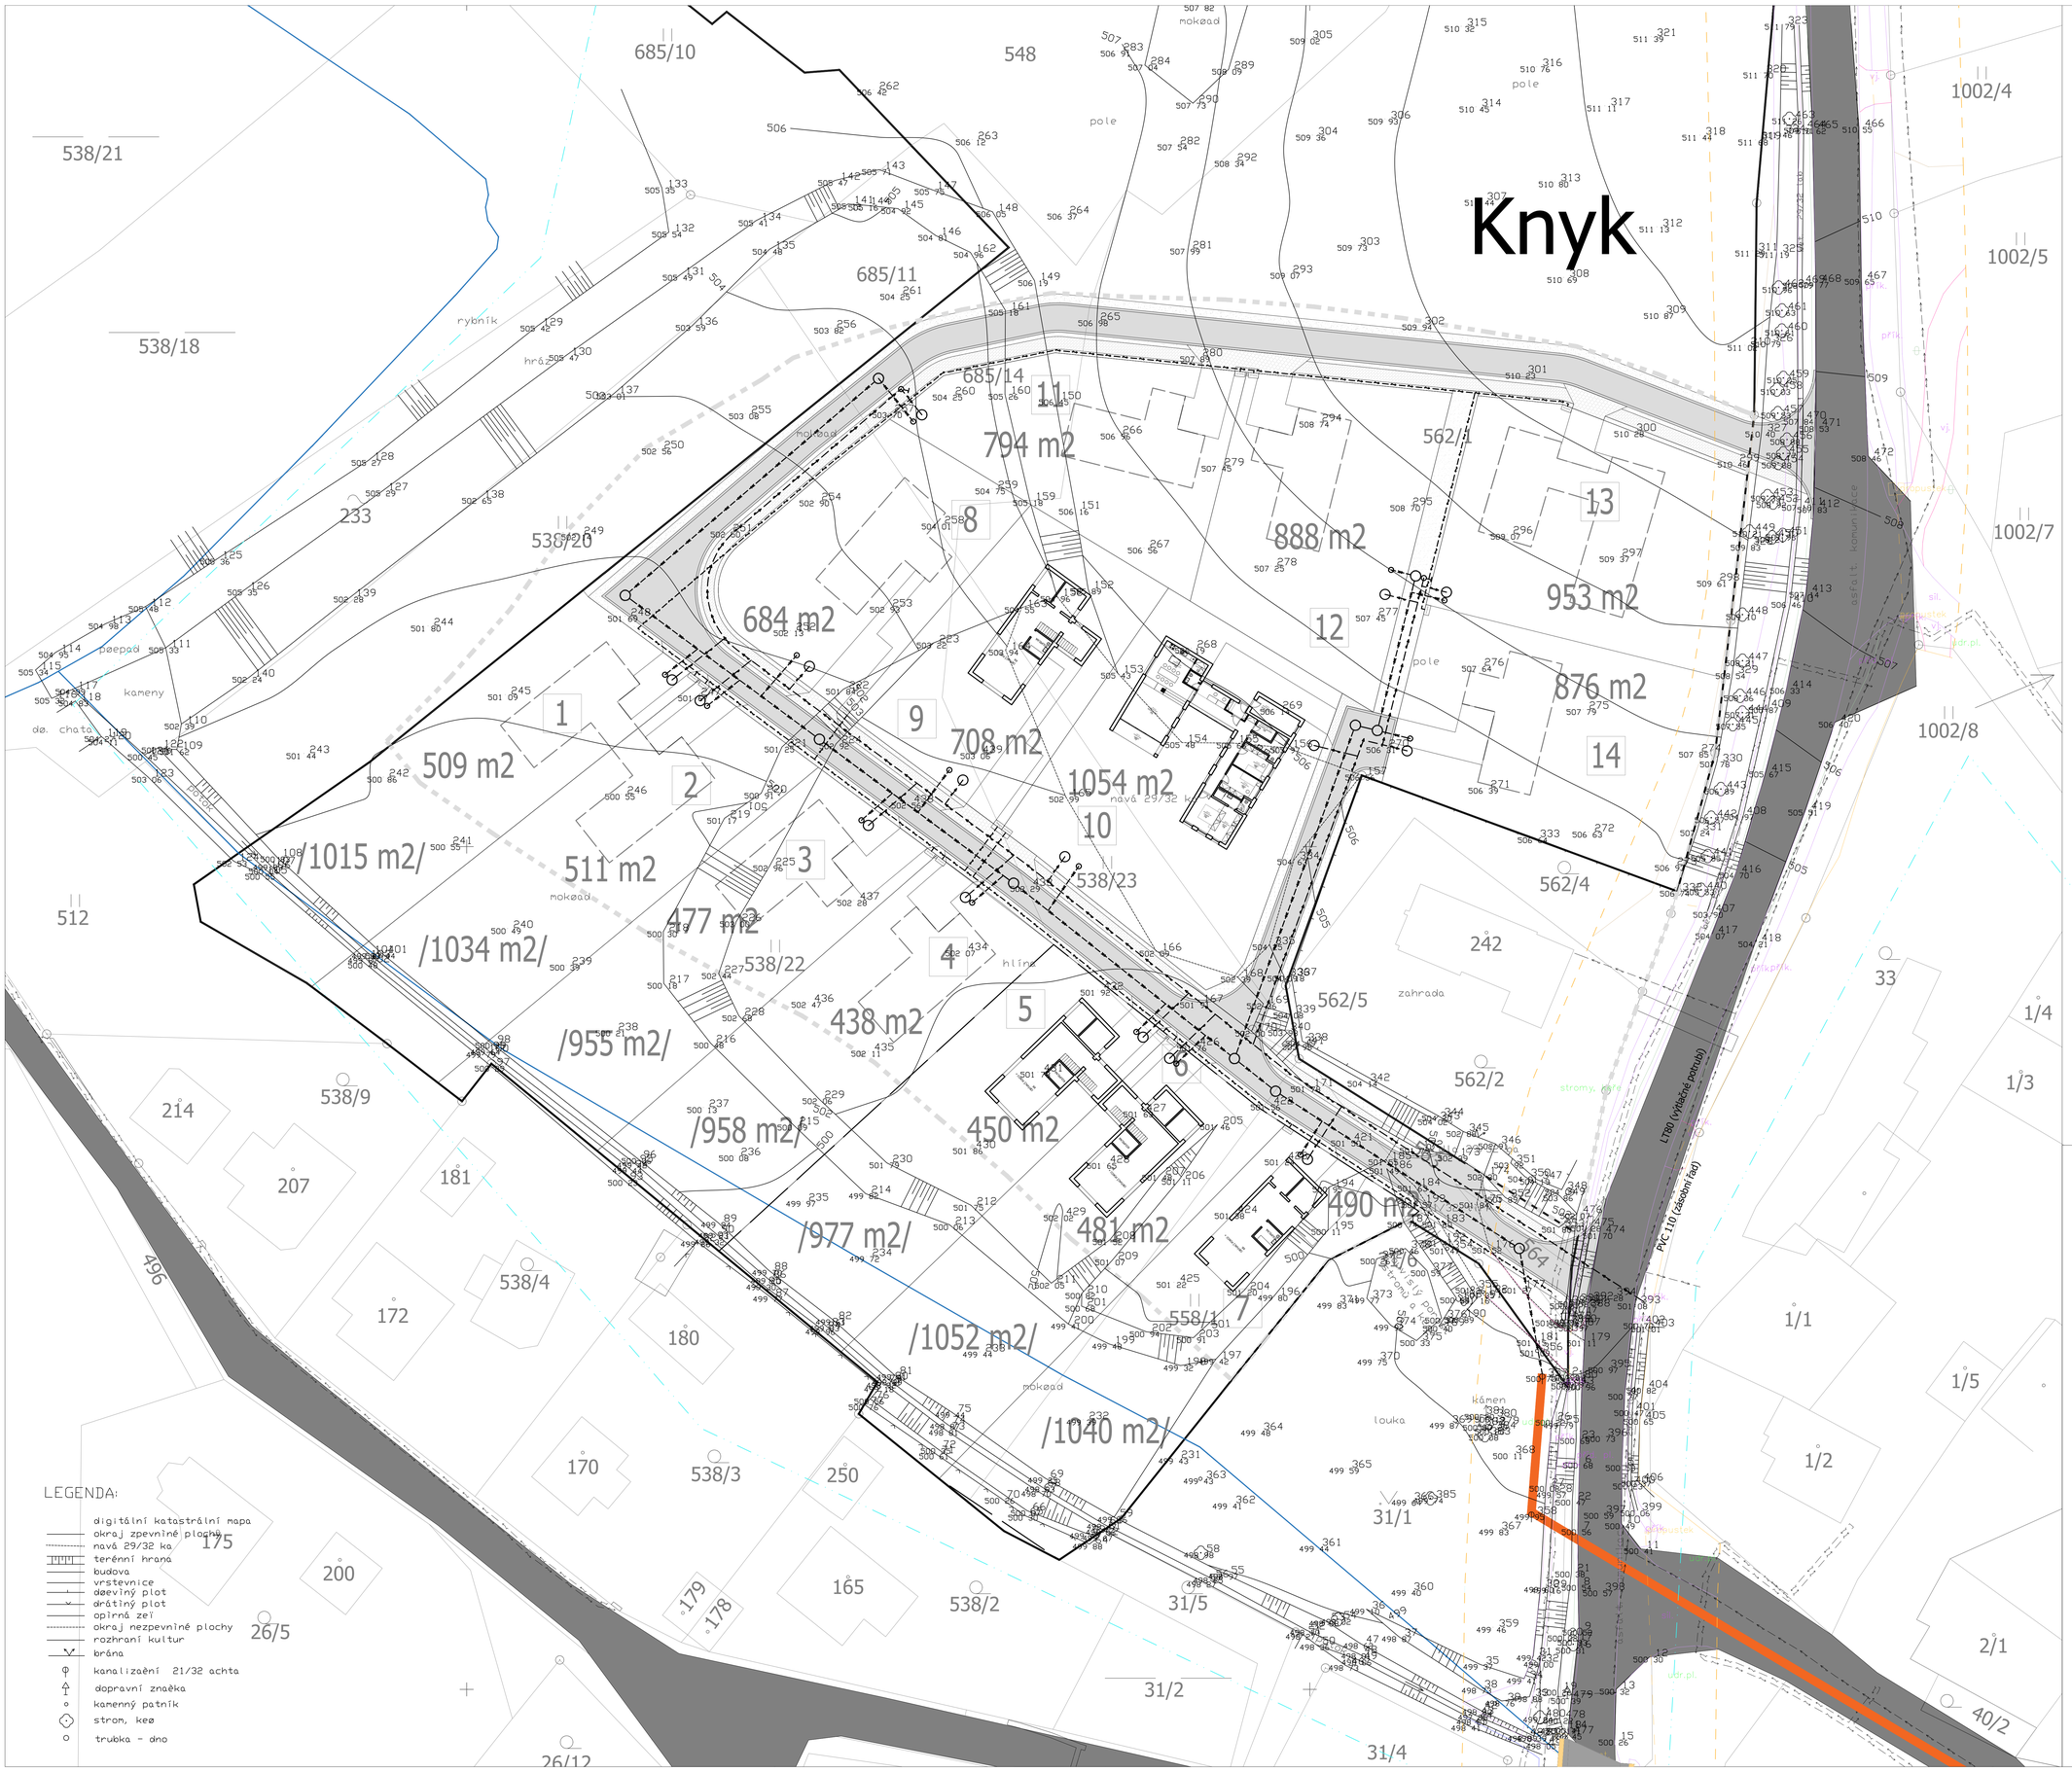

LEGENDA KOORDINAČNÍHO VÝKRESU SITUACE

a) koordinační situační výkres měřítko M 1 : 250

b) stávající stavby, dopravní a technická infrastruktura, křížení se stavbami technické a dopravní infrastruktury a souběhy s nimi v případě, kdy jsou stavby umístěny v ochranném pásmu stavby technické a dopravní infrastruktury, nebo je-li ohrožena bezpečnost

- STÁVAJÍCÍ NADZEMNÍ OBJEKTY BEZ ROZLIŠENÍ
- STÁVAJÍCÍ OPLOCENÍ BEZ SPECIFIKACE
- DOPRAVNÍ INFRASTRUKTURA - STÁVAJÍCÍ KOMUNIKACE - ZPEVNĚNÉ PLOCHY
  STÁVAJÍCÍ KOMUNIKACE, MÍSTNÍ KOMUNIKACE
- DOPRAVNÍ INFRASTRUKTURA - STÁVAJÍCÍ KOMUNIKACE - NEZPEVNĚNÉ PLOCHY
  NEZPEVNĚNÁ KOMUNIKACE - POLNÍ CESTA
- STÁVAJÍCÍ VODOVODNÍ ŘAD
- SDĚLOVACÍ VEDENÍ NADZEMNÍ
  NADZEMNÍ VEDENÍ CETIN
- ELEKTRICKÉ VEDENÍ
  NADZEMNÍ VEDENÍ NN
- ELEKTRICKÉ VEDENÍ
  PODZEMNÍ VEDENÍ NN
  OCHRANNÉ PÁSMO
- ELEKTRICKÉ VEDENÍ
  NADZEMNÍ VEDENÍ VN DO 35 kV
  OCHRANNÉ PÁSMO

c) hranice pozemků, parcelní čísla

- PARCELY STAVEBNÍKA

d) hranice řešeného území

- ZAKRESLENO V MAPOVÉM PODKLADU
  PÁSMO URČENÉ K ZÁSTAVBĚ RD

e) stávající výškopis a polohopis

- ZAKRESLENO V MAPOVÉM PODKLADU

f) stanovení nadmořské výšky prvního nadzemního podlaží u budov (± 0, 00) a výšky upraveného terénu; maximální výška staveb, nivelační a pevné body pro vytyčení stavby, definování výškové úrovně pro přelivy, koruny hrází apod.,

- stanovení nadmořské výšky prvního nadzemního podlaží u budov (± 0, 00) a výšky upraveného terénu
- maximální výška staveb
- nivelační a pevné body pro vytyčení stavby
- definování výškové úrovně pro přelivy, koruny hrází apod.,

g) vyznačení jednotlivých navržených nebo odstraňovaných staveb a technické infrastruktury, včetně napojení stavby na technickou infrastrukturu

- vyznačení jednotlivých navržených nebo odstraňovaných staveb
- NOVĚ NAVRŽENÁ SPLAŠKOVÁ KANALIZACE
- NOVĚ NAVRŽENÝ VODOVODNÍ ŘAD PVC 110
- PŘEDPOKLÁDANÁ TRASA EL VEDENÍ
- PILÍŘE RE
  V RÁMCI PD JSOU ŘEŠENY POUZE PILÍŘE PRO JISTIČE A ELEKTROMĚR
  VLASTNÍ ELEKTRIFIKACE JE ŘEŠENA SAMOSTATNOU PD PROVOZOVATELEM DISTRIBUČNÍ SOUSTAVY

h) navrhované komunikace a zpevněné plochy, napojení na dopravní infrastrukturu

- NOVÁ ÚČELOVÁ KOMUNIKACE
  ŠVOČNÁ KOMUNIKACE PRO POJEZD AUTOMOBILŮ NAD 3,5t
  ŠÍŘKA KOMUNIKACE 6m, JEDNOSMĚRNÁ
- KOMUNIKACE PRO PĚŠÍ
- SJEZD NA JEDNOTLIVÉ PARCELY
  SJEZDY NA PARCELU STAVEBNÍKA, SJEZD SPÁDOVÁN NA PARCELU STAVEBNÍKA
  DLAŽDĚNÝ SJEZD PRO POJEZD AUTOMOBILŮ NAD 3,5t
  KAMENNÁ DLAŽBA TL. 100 mm
  KLADECÍ VRSTVA DRCENÉ KAMENIVO FRAKCE 4-8 mm TL. 100 mm
  ROZNÁŠECÍ VRSTVA DRCENÉ KAMENIVO FRAKCE 16-32 mm TL. 150 mm
  NOSNÁ VRSTVA DRCENÉ KAMENIVO FRAKCE 0-64 mm TL. 200 mm

i) řešení vegetace

- OZELENĚNÁ PLOCHA DOTČENÁ VÝSTAVBOU
  ZPĚTNÉ ROZPROSTŘENÍ SKRYTÉ ORNICE
  OSETÍ TRAVNÍM SEMENEM
- STÁVAJÍCÍ ZELEŇ URČENÁ KE KÁCENÍ

j) okótované odstupy, včetně odstupů od souvisejících technologických objektů

- ŘEŠENO VÝKRESEM
  KOTY JSOU SOUČÁSTÍ MAPOVÉHO PODKLADU

k) maximální dočasné a trvalé zábory

- TRVALÉ ZÁBORY
  JEDNÁ SE O ZÁBOR V PROSTORU NAPOJENÍ VODOVODNÍHO ŘADU
  JEDNÁ SE O ZÁBOR V PROSTORU NAPOJENÍ KANALIZACE
- DOČASNÉ ZÁBORY
  JEDNÁ SE O ZÁBOR PRO PROVEDENÍ STAVBY MIMO PARCELY STAVEBNÍKA
  ZÁBOR BUDE ŘEŠEN DODAVATELEM STAVBY NA ZÁKLADĚ HARMONOGRAMU VÝSTAVBY

l) hranice staveniště s vyznačením vjezdu

- HRANICE STAVENIŠTĚ
- VJEZD NA STAVENIŠTĚ
  NAPOJENÍ NA ÚČELOVOU KOMUNIKACI

m) odstupové vzdálenosti včetně vymezení požárně nebezpečných prostorů, přístupové komunikace a nástupní plochy pro požární techniku a zdroje požární vody

- Odstupové vzdálenosti včetně vymezení požárně nebezpečných prostorů
  STAVEBNÍ OBJEKTY DOPRAVNÍ A TECHNICKÉ INFRASTRUKTURY NEMAJÍ POŽÁRNĚ NEBEZPEČNÝ PROSTOR
- Přístupové komunikace a nástupní plochy pro požární techniku
  PŘÍSTUPOVÉ KOMUNIKACE, MÍSTNÍ ÚČELOVÁ KOMUNIKACE
  NÁSTUPNÍ PLOCHY PRO PLÁNOVANOU INDIVIDUÁLNÍ RODINNÉ BYDLENÍ NEJSOU ZŘIZOVÁNY
- OSAZENÍ NOVÉHO POŽÁRNÍHO HYDRANTU DN 80 NA POTRUBÍ PVC 110
  OSAZENÍ NOVÉHO PODZEMNÍHO HYDRANTU
  HYDRANT PRO ZÁSOBOVÁNÍ LOKALITY POŽÁRNÍ VODOU
  HYDRANT SLOUŽÍ PRO ZÁSOBOVÁNÍ OBCE POŽÁRNÍ VODOU
  STÁVAJÍCÍ HYDRANT JE VZDÁLEN CCA 900 m OD PLÁNOVANÉ LOKALITY

PROJEKTANT: Ing. Jaroslav Pfleger, Tyršova 542, Jablonné v Podještědí	PROJEKTANT A ZAVITEL Ing. Jaroslav Pfleger ČKAIT: 0501363 Tyršova 542, Jablonné v P. IČ: 882 217 92 T: 602 429 314 E: jaroslav.pfleger@centrum.cz
VYPRACOVAL: Ing. Jaroslav Pfleger, Tyršova 542, Jablonné v Podještědí	
DIZAJNÉR: Miroslav Štěpánek	
STAVEBNÍK: 3K-Profil s.r.o., Knyk 230, 580 01 Knyk IČ: 27542653 DIČ: CZ27542653	
NÁZEV STAVBY: Výstavba dopravní a technické infrastruktury pro plánovanou lokalitu RD, Výstavba 5 ks rodinných domů, na p.č. 558/1, 538/22, 538/23, 562/1, 562,4, 685/14 v k.ú. Knyk	PARÉ Č.: 1 2 3 4 5 6
STAVEBNÍ OBJEKT: SO11 - výstavba dopravní a technické infrastruktury SO01 - výstavba RD	STUPEŇ PD: DUR+DSP DATUM: 07.2025
ČÁST: C Situační výkresy	ZAKÁZKA ČÍSLO: 701.25
C - KOORDINAČNÍ SITUAČNÍ VÝKRES	MĚŘÍTKO: 1 : 250 ČÍSLO VÝKRESU: C 3